売買代金内訳

令和8年10月10日

宮崎市下北方町常盤元988番地1
株式会社グローバル


宮崎市大字熊野字宮ケ田瀬

「野村先生」

:5233番2	18,800,000円
:5228番	2,290,000円
:5233番3	833,000円
:5231番2の一部(25.57㎡)	399,000円
計	22,322,000円

「調剤薬局」

:5231番2の一部（203.92㎡）	3,182,000円

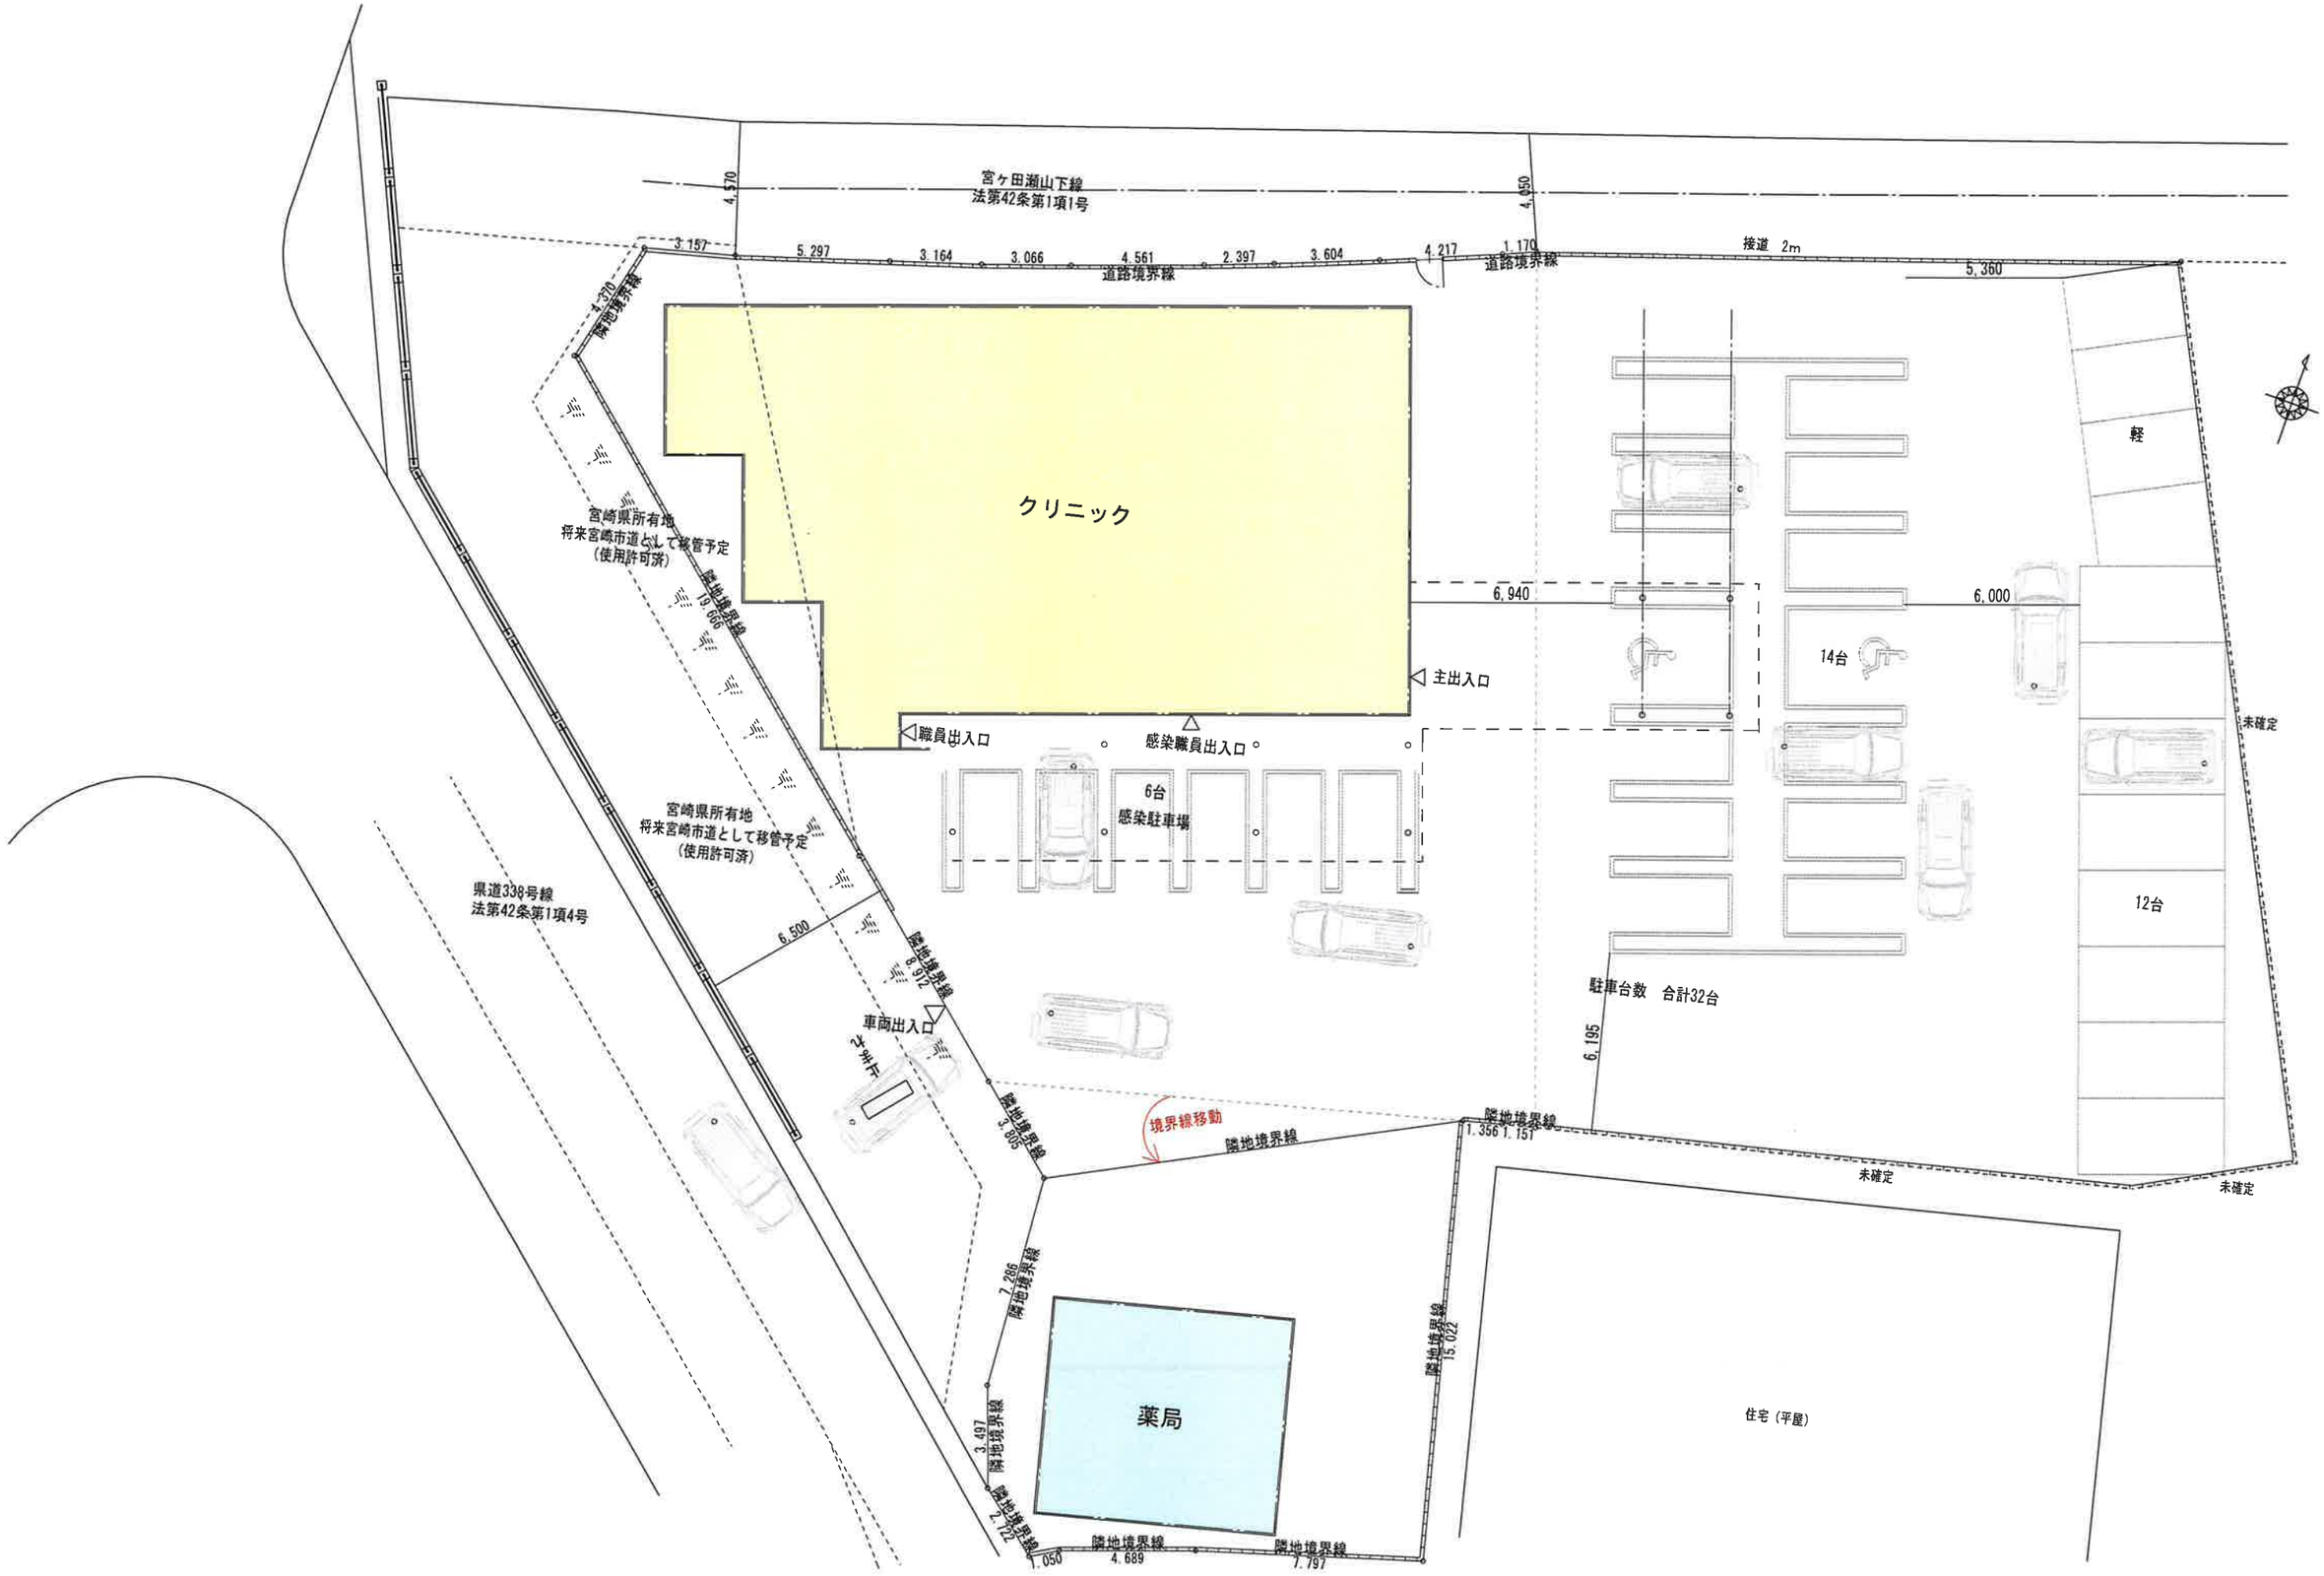

PROJECT （仮称）宮崎市熊野クリニック新築工事


TITLE 配置図

AAO建築アトリエ
一級建築士登録 289104 足立梨

DATE 2026/09/03
SCALE 1/200
NO 1

表示年月日：２０２６／０６／０３

イ 5260-1
ロ 5260
ハ 5246-2
ニ 5242-2

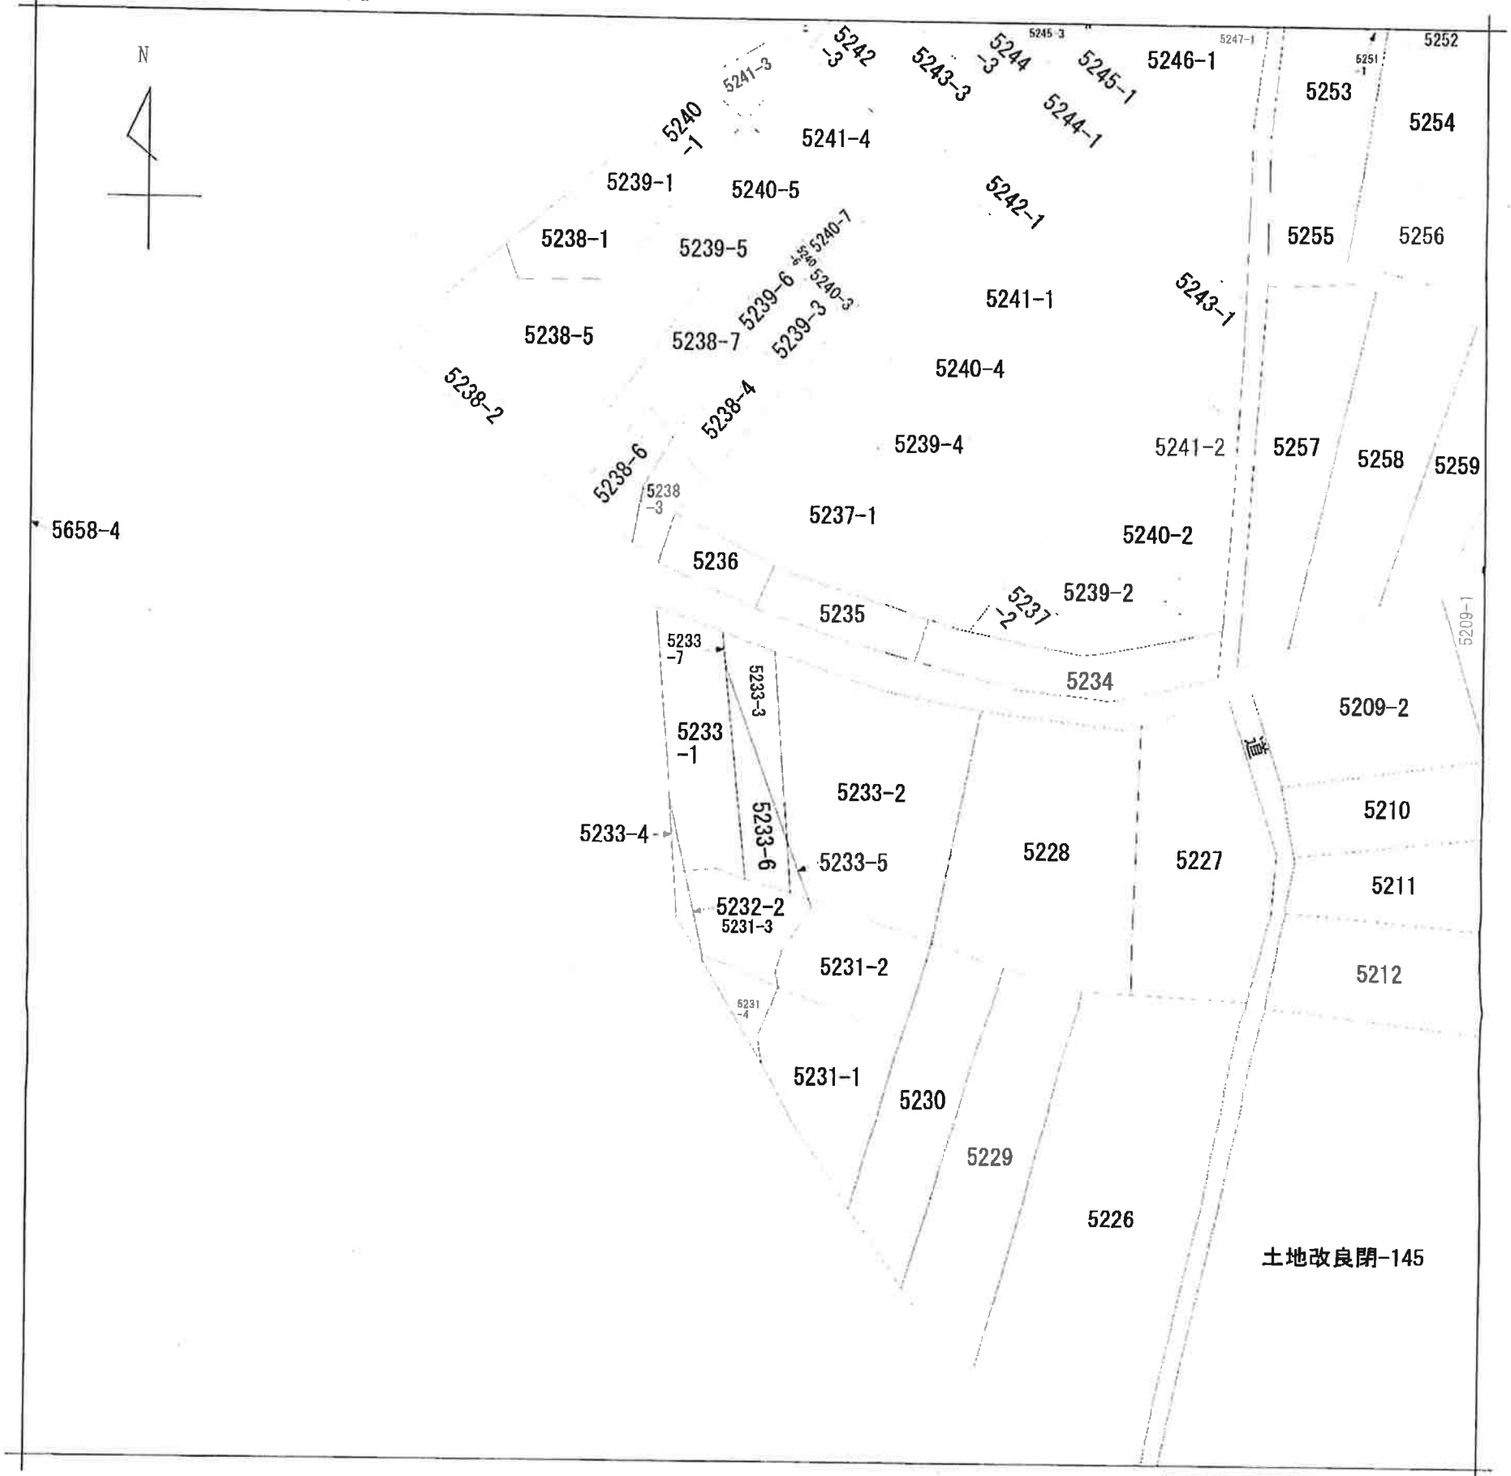

地番区域見出	大字熊野

A 大字熊野

請求部分	所在	宮崎市大字熊野字宮ケ田瀬					地番	5233番3		
出力縮尺	縮尺不明	精度区分		座標系番号又は記号		分類	地図に準ずる図面		種類	旧土地台帳附属地図
作成年月日	明治20年			備付年月日（原図）				補記事項		

(1/1)

座　標　求　積　表

地　番	5228（確定）			
測　点	Xn	Yn	(Xn+1 － Xn-1)Yn	距　離
K117	-128493.531	39860.871	-1071579.795093	32.39
701	-128522.152	39876.050	-1274478.434050	5.99
KS109	-128525.492	39871.067	-189586.923585	6.15
703	-128526.907	39865.078	-145946.050558	9.54
K151	-128529.153	39855.804	1033899.411564	29.87
K122	-128500.966	39845.901	1157045.273238	2.16
K121	-128500.115	39847.889	100456.528169	4.05
K120	-128498.445	39851.580	118877.263140	2.95
K119	-128497.132	39854.225	126577.018600	4.03
K118	-128495.269	39857.800	143527.937800	3.52
		倍　面　積	-1207.770775	
		面　積	603.885387	
		地　積	603.88　㎡	
		坪　数	182.67	

地　番	5231-2の一部			
測　点	Xn	Yn	(Xn+1 － Xn-1)Yn	距　離
K149	-128529.767	39853.373	98995.778532	16.32
H3	-128533.901	39837.581	-263645.111058	3.80
H2	-128536.385	39840.464	164700.478176	14.50
		倍　面　積	51.145650	
		面　積	25.572825	
		地　積	25.57　㎡	
		坪　数	7.73	

地　番	5233-2			
測　点	Xn	Yn	(Xn+1 － Xn-1)Yn	距　離
H3	-128533.901	39837.581	-67086.486404	16.32
K149	-128529.767	39853.373	178423.550921	1.35
K150	-128529.424	39854.685	24470.776590	1.15
K151	-128529.153	39855.804	1134216.470232	29.87
K122	-128500.966	39845.901	1104767.451126	1.17
K123	-128501.427	39844.825	-81960.805025	4.21
K124	-128503.023	39840.921	-115857.398268	3.60
K125	-128504.335	39837.564	-85690.600164	2.39
K126	-128505.174	39835.318	-94011.350480	4.56
K127	-128506.695	39831.018	-99936.024162	3.06
K128	-128507.683	39828.115	-76868.261950	3.16
K129	-128508.625	39825.094	-100518.537256	5.29
K130	-128510.207	39820.038	-774818.299404	20.88
H4	-128528.083	39830.830	-943751.686020	8.91
		倍　面　積	1378.799736	
		面　積	689.399868	
		地　積	689.39　㎡	
		坪　数	208.54	

地　番	5233-3			
測　点	Xn	Yn	(Xn+1 － Xn-1)Yn	距　離
H5	-128515.245	39815.932	-680095.934492	19.66
H4	-128528.083	39830.830	200667.721540	20.88
K130	-128510.207	39820.038	680166.069078	3.15
H6	-128511.002	39816.982	-200597.955316	4.37
		倍　面　積	139.900810	
		面　積	69.950405	
		地　積	69.95　㎡	
		坪　数	21.15	

本図面は境界立会等を行っていないため仮図です。
境界立会の結果、辺長・面積等が変更になる可能性が
ありますので取り扱いには十分にご注意ください。



図面名称	参考図		
所　在	宮崎市大字熊野字宮ケ田瀬		
縮　尺	1：300	作成年月日	令和 8年 10月 10日

宮崎市大字恒久1516番地3
ディアコート吉永202号
土地家屋調査士　　柚木正大

座　標　求　積　表


地　番	(K)5228				
No.	標識	Xn	Yn	辺　長	点間No
504		-128493.524	39860.917	32.413	505
505		-128522.171	39876.083	5.950	507
507		-128525.486	39871.142	6.214	506
506		-128526.924	39865.096	9.555	K151
K151		-128529.153	39855.804	29.876	K122
K122		-128500.966	39845.901	7.084	501
501		-128498.079	39852.371	8.040	H-CB2
H-CB2		-128494.355	39859.497	1.645	504
			倍　面　積	-1210.955654	
			面　積	605.477827	
			地　積	605.47	㎡

地　番	5233-2				
No.	標識	Xn	Yn	辺　長	点間No
H3		-128533.901	39837.581	16.324	K149
K149		-128529.767	39853.373	1.356	K150
K150		-128529.424	39854.685	1.151	K151
K151		-128529.153	39855.804	29.876	K122
K122		-128500.966	39845.901	1.170	K123
K123		-128501.427	39844.825	4.217	K124
K124		-128503.023	39840.921	3.604	K125
K125		-128504.335	39837.564	2.397	K126
K126		-128505.174	39835.318	4.561	K127
K127		-128506.695	39831.018	3.066	K128
K128		-128507.683	39828.115	3.164	K129
K129		-128508.625	39825.094	5.297	K130
K130		-128510.207	39820.038	20.881	H4
H4		-128528.083	39830.830	8.912	H3
			倍　面　積	1378.799736	
			面　積	689.399868	
			地　積	689.39	㎡

地　番	5233-3				
No.	標識	Xn	Yn	辺　長	点間No
H5		-128515.245	39815.932	19.666	H4
H4		-128528.083	39830.830	20.881	K130
K130		-128510.207	39820.038	3.157	H6
H6		-128511.002	39816.982	4.370	H5
			倍　面　積	139.900810	
			面　積	69.950405	
			地　積	69.95	㎡

地　番	5231-2				
No.	標識	Xn	Yn	辺　長	点間No
P55		-128548.675	39844.251	1.050	K157
K157		-128548.151	39845.162	4.689	K158
K158		-128546.588	39849.583	7.797	K159
K159		-128544.333	39857.047	15.022	K149
K149		-128529.767	39853.373	16.324	H3
H3		-128533.901	39837.581	3.805	H2
H2		-128536.385	39840.464	7.286	H1
H1		-128543.654	39840.968	3.498	R6
R6		-128546.948	39842.146	2.722	P55
			倍　面　積	458.985258	
			面　積	229.492629	
			地　積	229.49	㎡

本図面は境界立会等を行っていないため仮図です。
境界立会の結果、辺長・面積等が変更になる可能性がありますので取り扱いには十分にご注意ください。

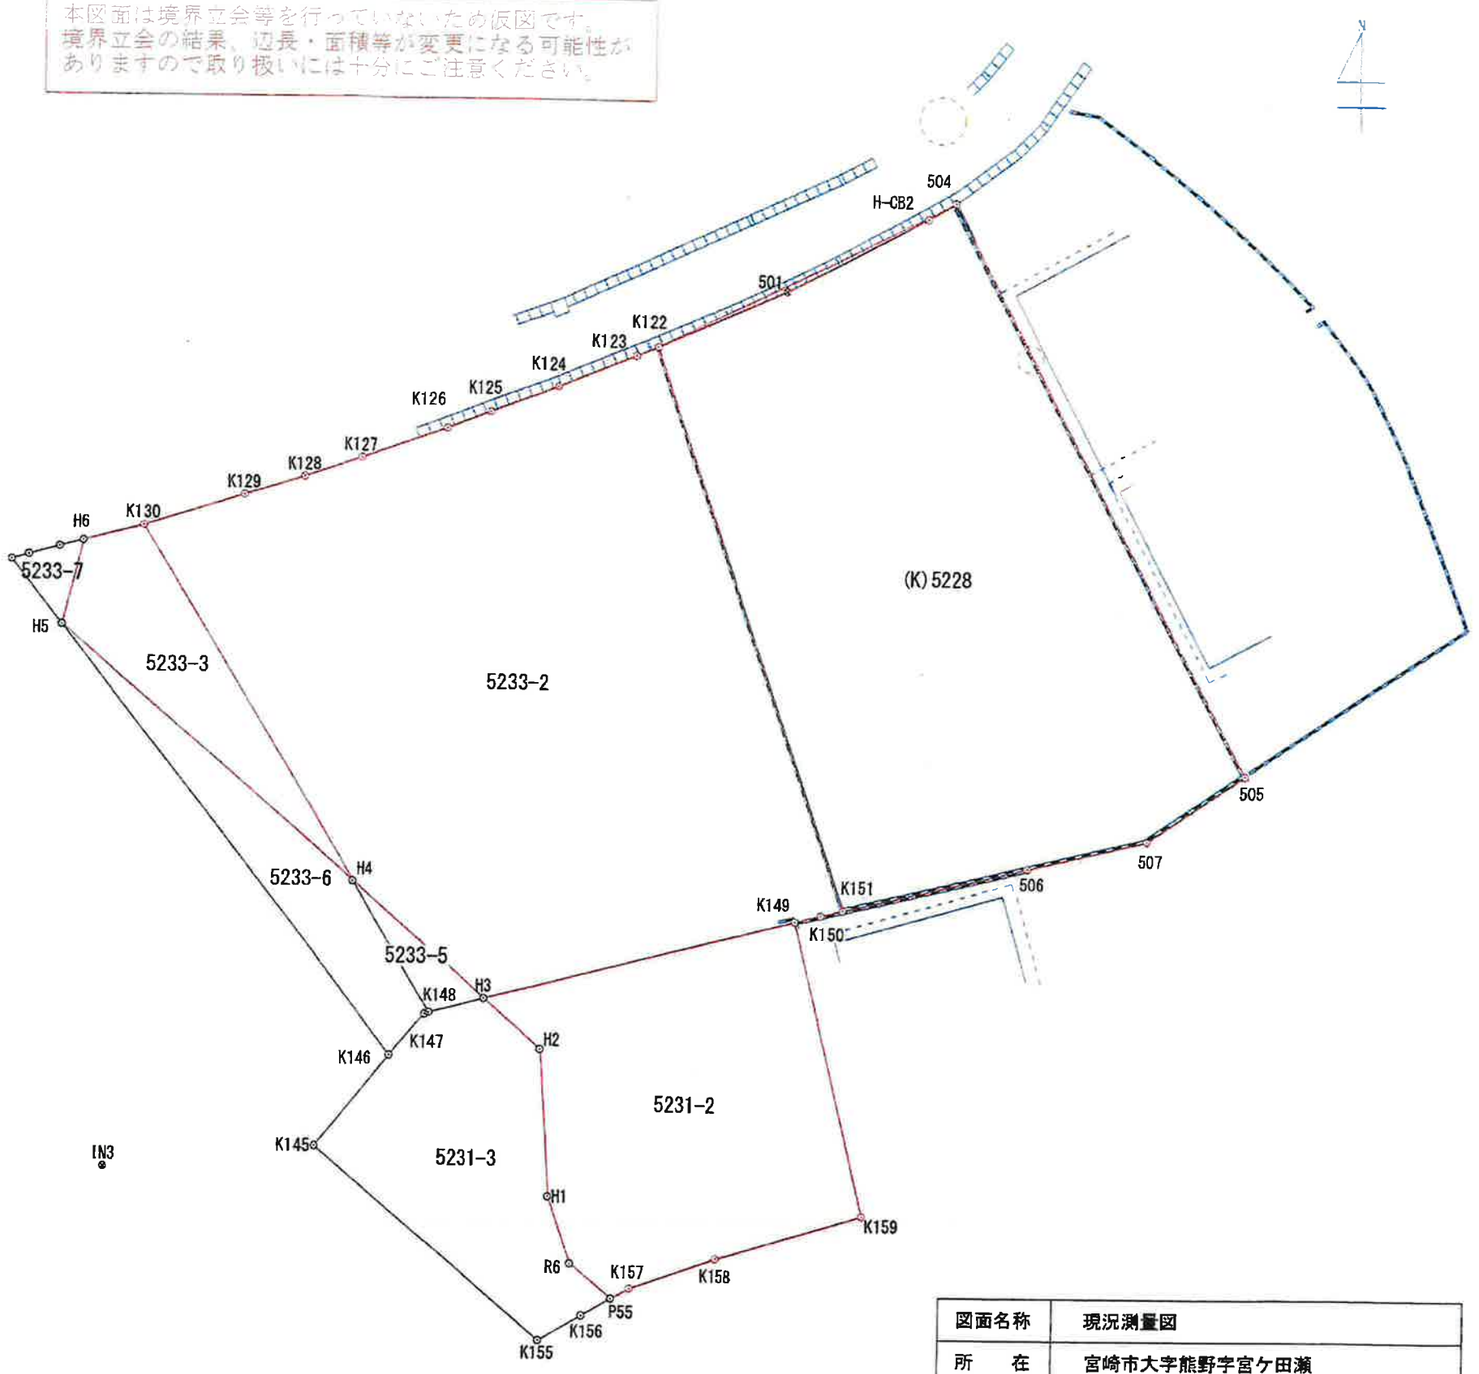

図面名称	現況測量図		
所　在	宮崎市大字熊野字宮ケ田瀬		
縮　尺	1：250	作成年月日	令和 8 年 8月14日

宮崎市大字恒久1516番地3
ディアコート吉永202号
土地家屋調査士　　柚木正大